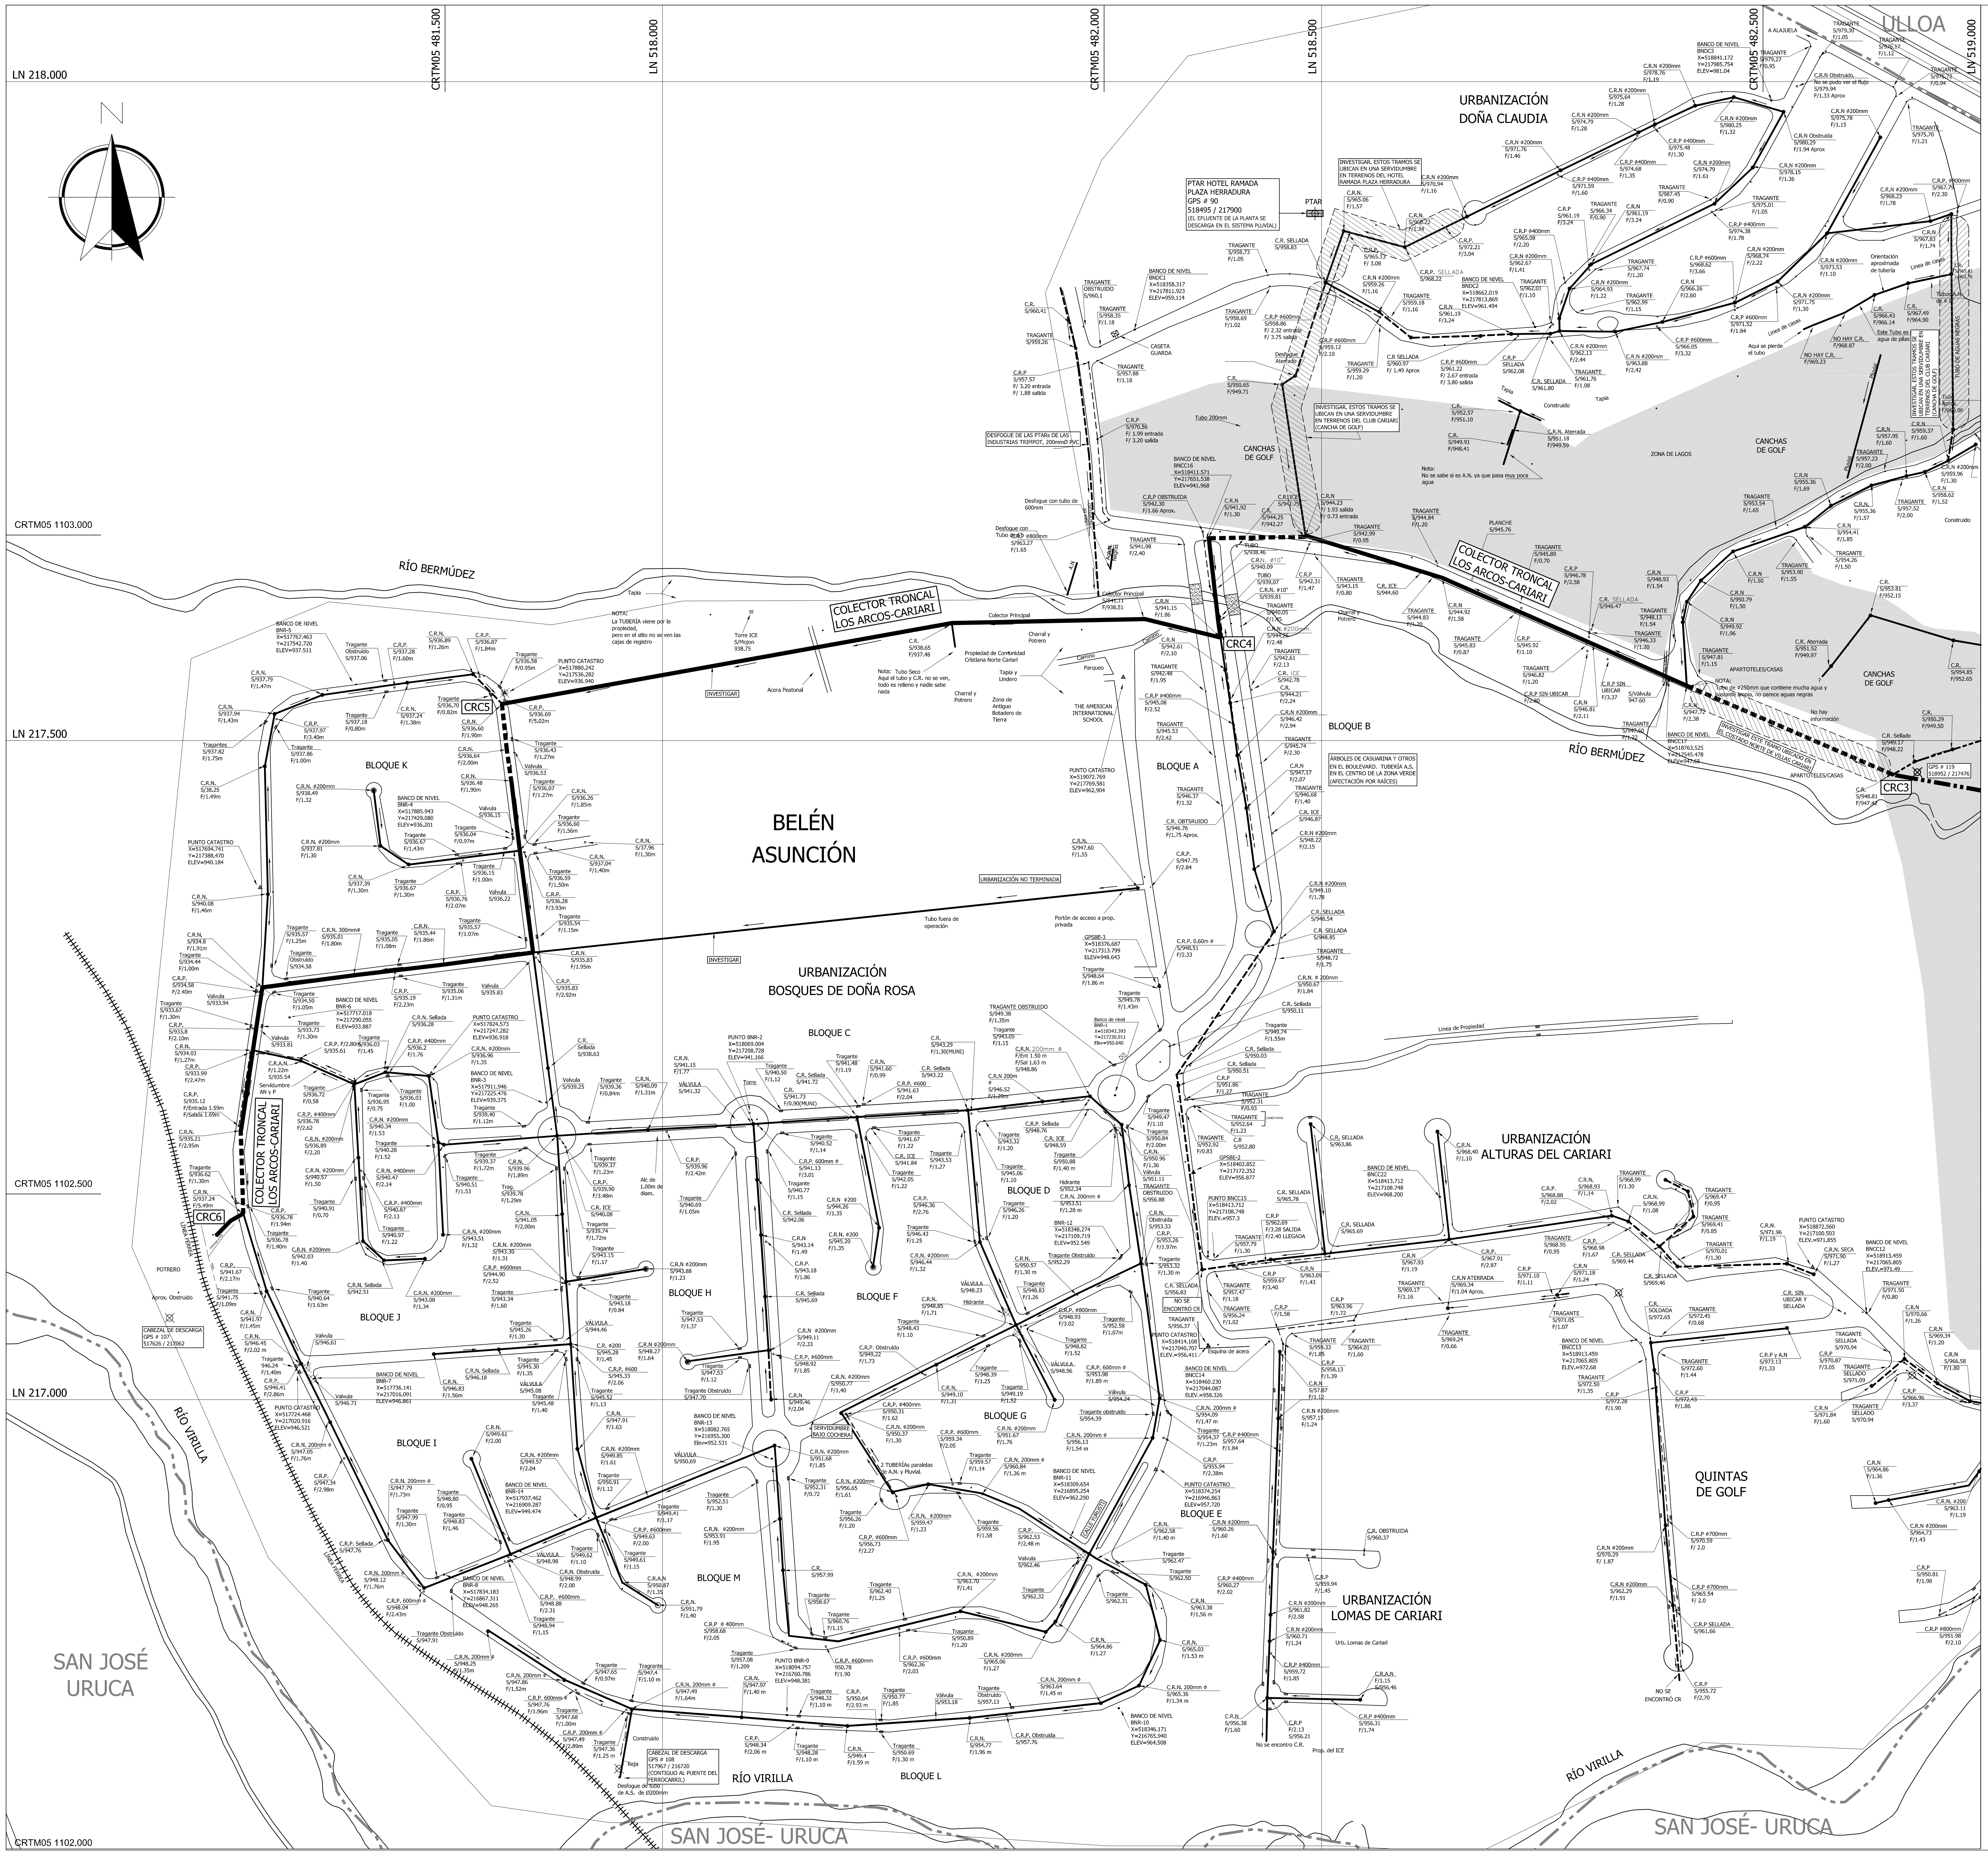

MUNICIPALIDAD DE BELÉN

CONSULTORES:

CONCESA
Consultores Centroamericanos en Ingeniería S.A.

Ing. HERBERT FARRER C.
Ing. LUIS PAULINO PICADO B.
Ing. SAUL TREJOS B.

PROYECTO:

PLAN MAESTRO DE RECOLECCIÓN,
TRATAMIENTO Y DISPOSICIÓN
DE LAS AGUAS RESIDUALES
DEL CANTÓN DE BELÉN (PMASB)

CONTENIDO:
CARIARI: INFRAESTRUCTURA EXISTENTE DE ALCANTARILLADO SANITARIO:
SECTOR OESTE.
LEVANTAMIENTO DEL AYA COMPLEMENTADO CON OBSERVACIONES DE CONCESA

ESCALA:	1 : 7500
SISTEMA DE COORDENADAS:	LAMBERT NORTE y CRTM-05
FECHA:	ENERO 2011
LÁMINA:	G-08

SIMBOLOGÍA

━━━	TUBERÍA AGUAS SANITARIAS IDENTIFICADA POR AYA
━ ━ ━	TUBERÍA AGUAS SANITARIAS IDENTIFICADA POR CONSULTORES CONCESA (ADICIONAL)
━ ‐ ━	TUBERÍA ROTA, FUERA DE SERVICIO
– – –	TUBERÍA AGUAS PLUVIALES
▨	TUBERÍA, ÁREA, ETC. A INVESTIGAR
PTAR ▨	UBICACIÓN PLANTA DE TRATAMIENTO
▲	PUNTOS GPS Y PUNTOS CATASTRO
▭	BANCOS DE NIVEL(BN)
◎	PI's
CRA#	CAJA DE REGISTRO COLECTOR TRONCAL LOS ARCOS
CRC#	CAJA DE REGISTRO COLECTOR TRONCAL CARIARI
C.R.P S/972.28 F/1.90 ○	CAJA DE REGISTRO DEL ALCANTARILLADO PLUVIAL
C.R.N S/968.99 F/1.08 ●	CAJA DE REGISTRO DEL ALCANTARILLADO SANITARIO
⊠	CAJA DE REGISTRO
⋈	VÁLVULAS
A.S.	ALCANTARILLADO SANITARIO
PTAR	PLANTA DE TRATAMIENTO DE AGUAS RESIDUALES
PMASB	PLAN MAESTRO ALCANTARILLADO SANITARIO BELÉN
≈	RÍO ó QUEBRADA
▒	CAMPO DE GOLF
━ ▪ ▪ ━	LÍMITE DISTRITAL
LN	SISTEMA DE COORDENADAS LAMBERT NORTE
CRTM05	SISTEMA DE COORDENADAS TRANVERSAL MERCATOR 2005

NOTAS:

1-LA EXPRESION (MUNI) CORRESPONDE A DATOS SUMINISTRADOS POR LA MUNICIPALIDAD.

2-LA TOTALIDAD DE ESTAS REDES DEBE INVESTIGARASE, TODA VEZ QUE EXISTEN CAJAS DE REGISTRO TAPADAS Y OTRAS ATERRADAS INTERNAMENTE, ASÍ COMO TRAMOS INTERRUMPIDOS EN ESTOS PLANOS.

3-VER OTRAS ÁREAS CON RED DE ALCANTARILLADO SANITARIO EN LA LÁMINA G-10.

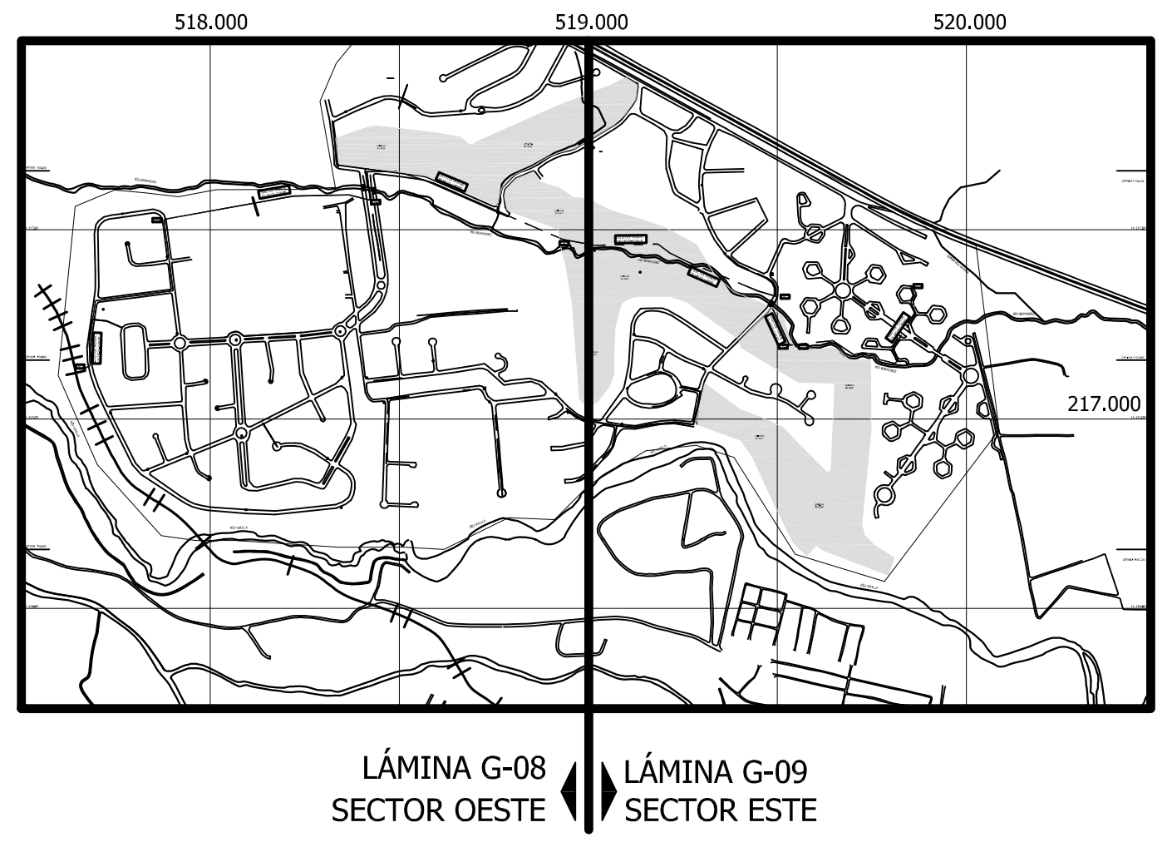

UBICACIÓN GEOGRÁFICA

HOJA SAN ANTONIO (COORDENADAS LAMBERT NORTE) ESCALA 1:20000