Planta — jardín de lluvia (sitio SBN-01, 5,0 × 5,0 m)

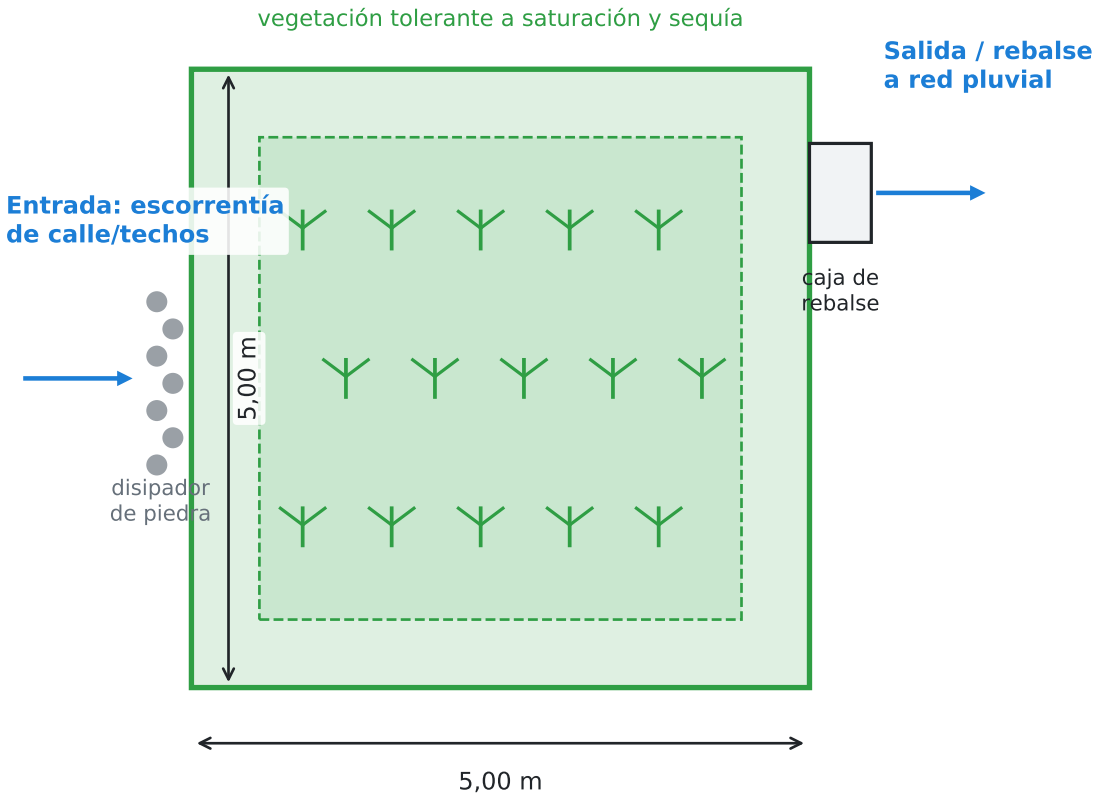
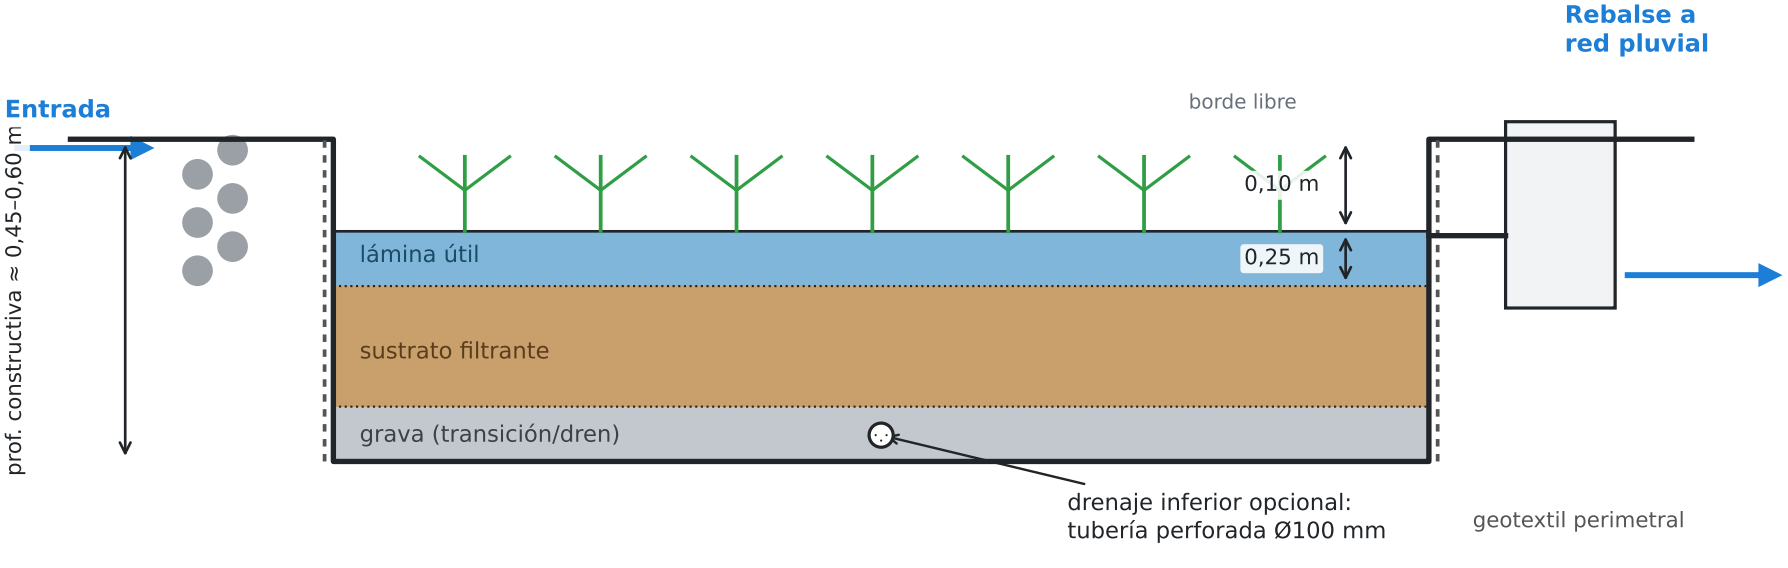
Sección transversal — capas constructivas