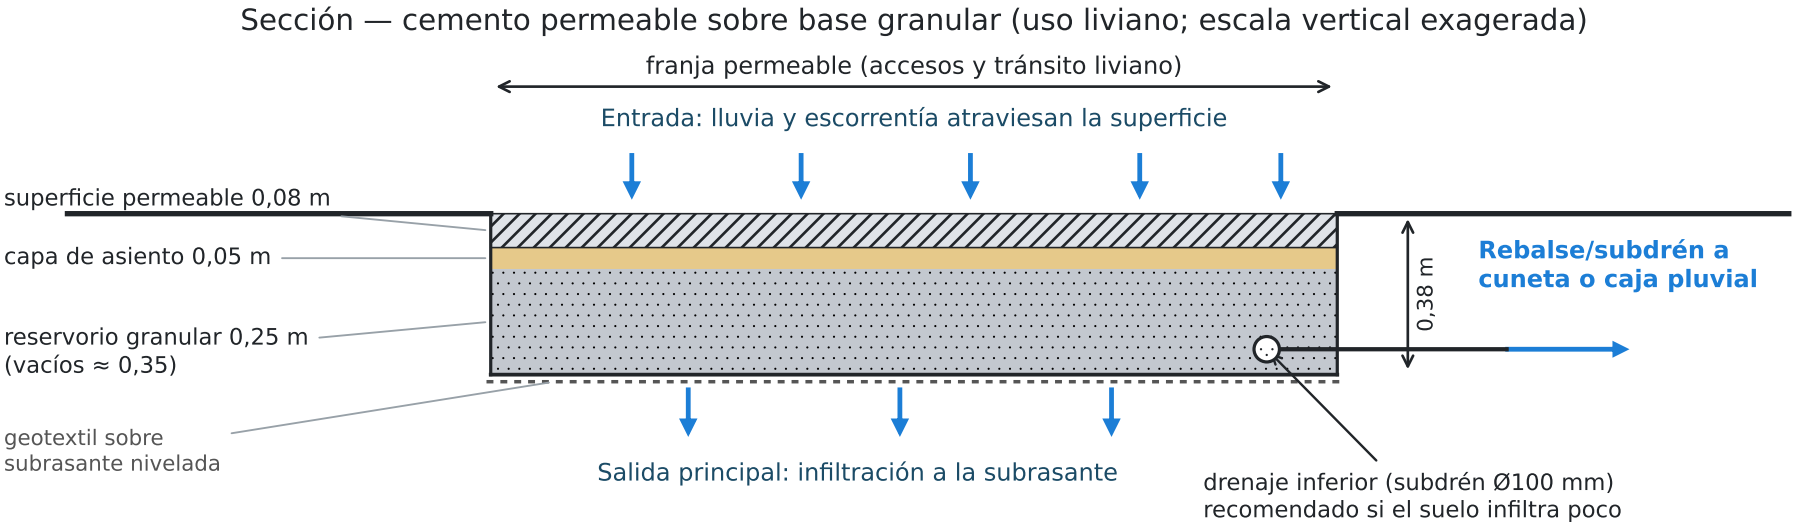
Sección — cemento permeable sobre base granular (uso liviano; escala vertical exagerada)
franja permeable (accesos y tránsito liviano)
Entrada: lluvia y escorrentía atraviesan la superficie
superficie permeable 0,08 m
capa de asiento 0,05 m
reservorio granular 0,25 m
(vacíos ≈ 0,35)
geotextil sobre
subrasante nivelada
0,38 m
Rebalse/subdrén a
cuneta o caja pluvial
Salida principal: infiltración a la subrasante
drenaje inferior (subdrén Ø100 mm)
recomendado si el suelo infiltra poco
pendiente transversal ≤ 2 %; sin entrada de sedimentos finos durante la obra