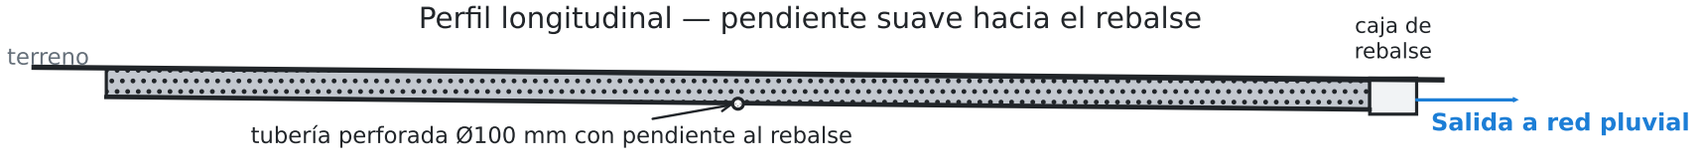
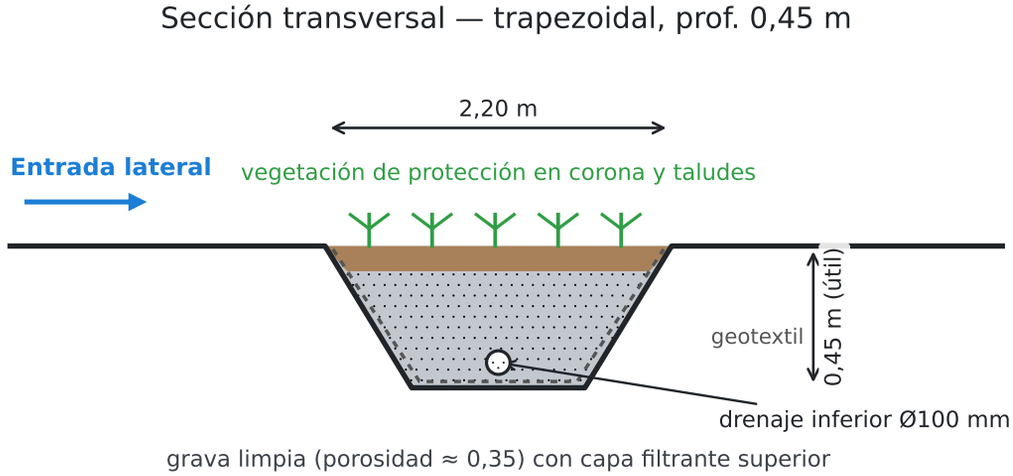

Planta — zanja infiltrante SBN-16 (70 m × 2,2 m)
Entrada distribuida: escorrentía lateral del corredor
Rebalse aguas abajo a red pluvial
2,2 m
70,0 m


Perfil longitudinal — pendiente suave hacia el rebalse
terreno
caja de rebalse
tubería perforada Ø100 mm con pendiente al rebalse
Salida a red pluvial


Sección transversal — trapezoidal, prof. 0,45 m
2,20 m
Entrada lateral
vegetación de protección en corona y taludes
geotextil
0,45 m (útil)
drenaje inferior Ø100 mm
grava limpia (porosidad ≈ 0,35) con capa filtrante superior